Stadt Liebstadt

Vorhabenbezogener Bebauungsplan „Solarpark Waltersdorf“

Planteil D: Vorhaben- Erschließungsplan

Planungsstand	**E N T W U R F**
Planfassung	19.12.2025
Stadt	Liebstadt
Vorhabenträger	SOLARPARK WALTERSDORF GMBH & CO.KG Waltersdorfer Str. 1 01825 Liebstadt
Auftragnehmer	LANDSCHAFTSARCHITEKTUR PANSE GBR Martin-Hoop-Str.12, 02625 Bautzen Tel.: 03591/52930, Fax: 03591/529329

VORHABEN- UND ERSCHLIESSUNGSPLAN
ZUM vB-PLAN "SOLARPARK WALTERSDORF" - SO 1 (M 1: 2.000)

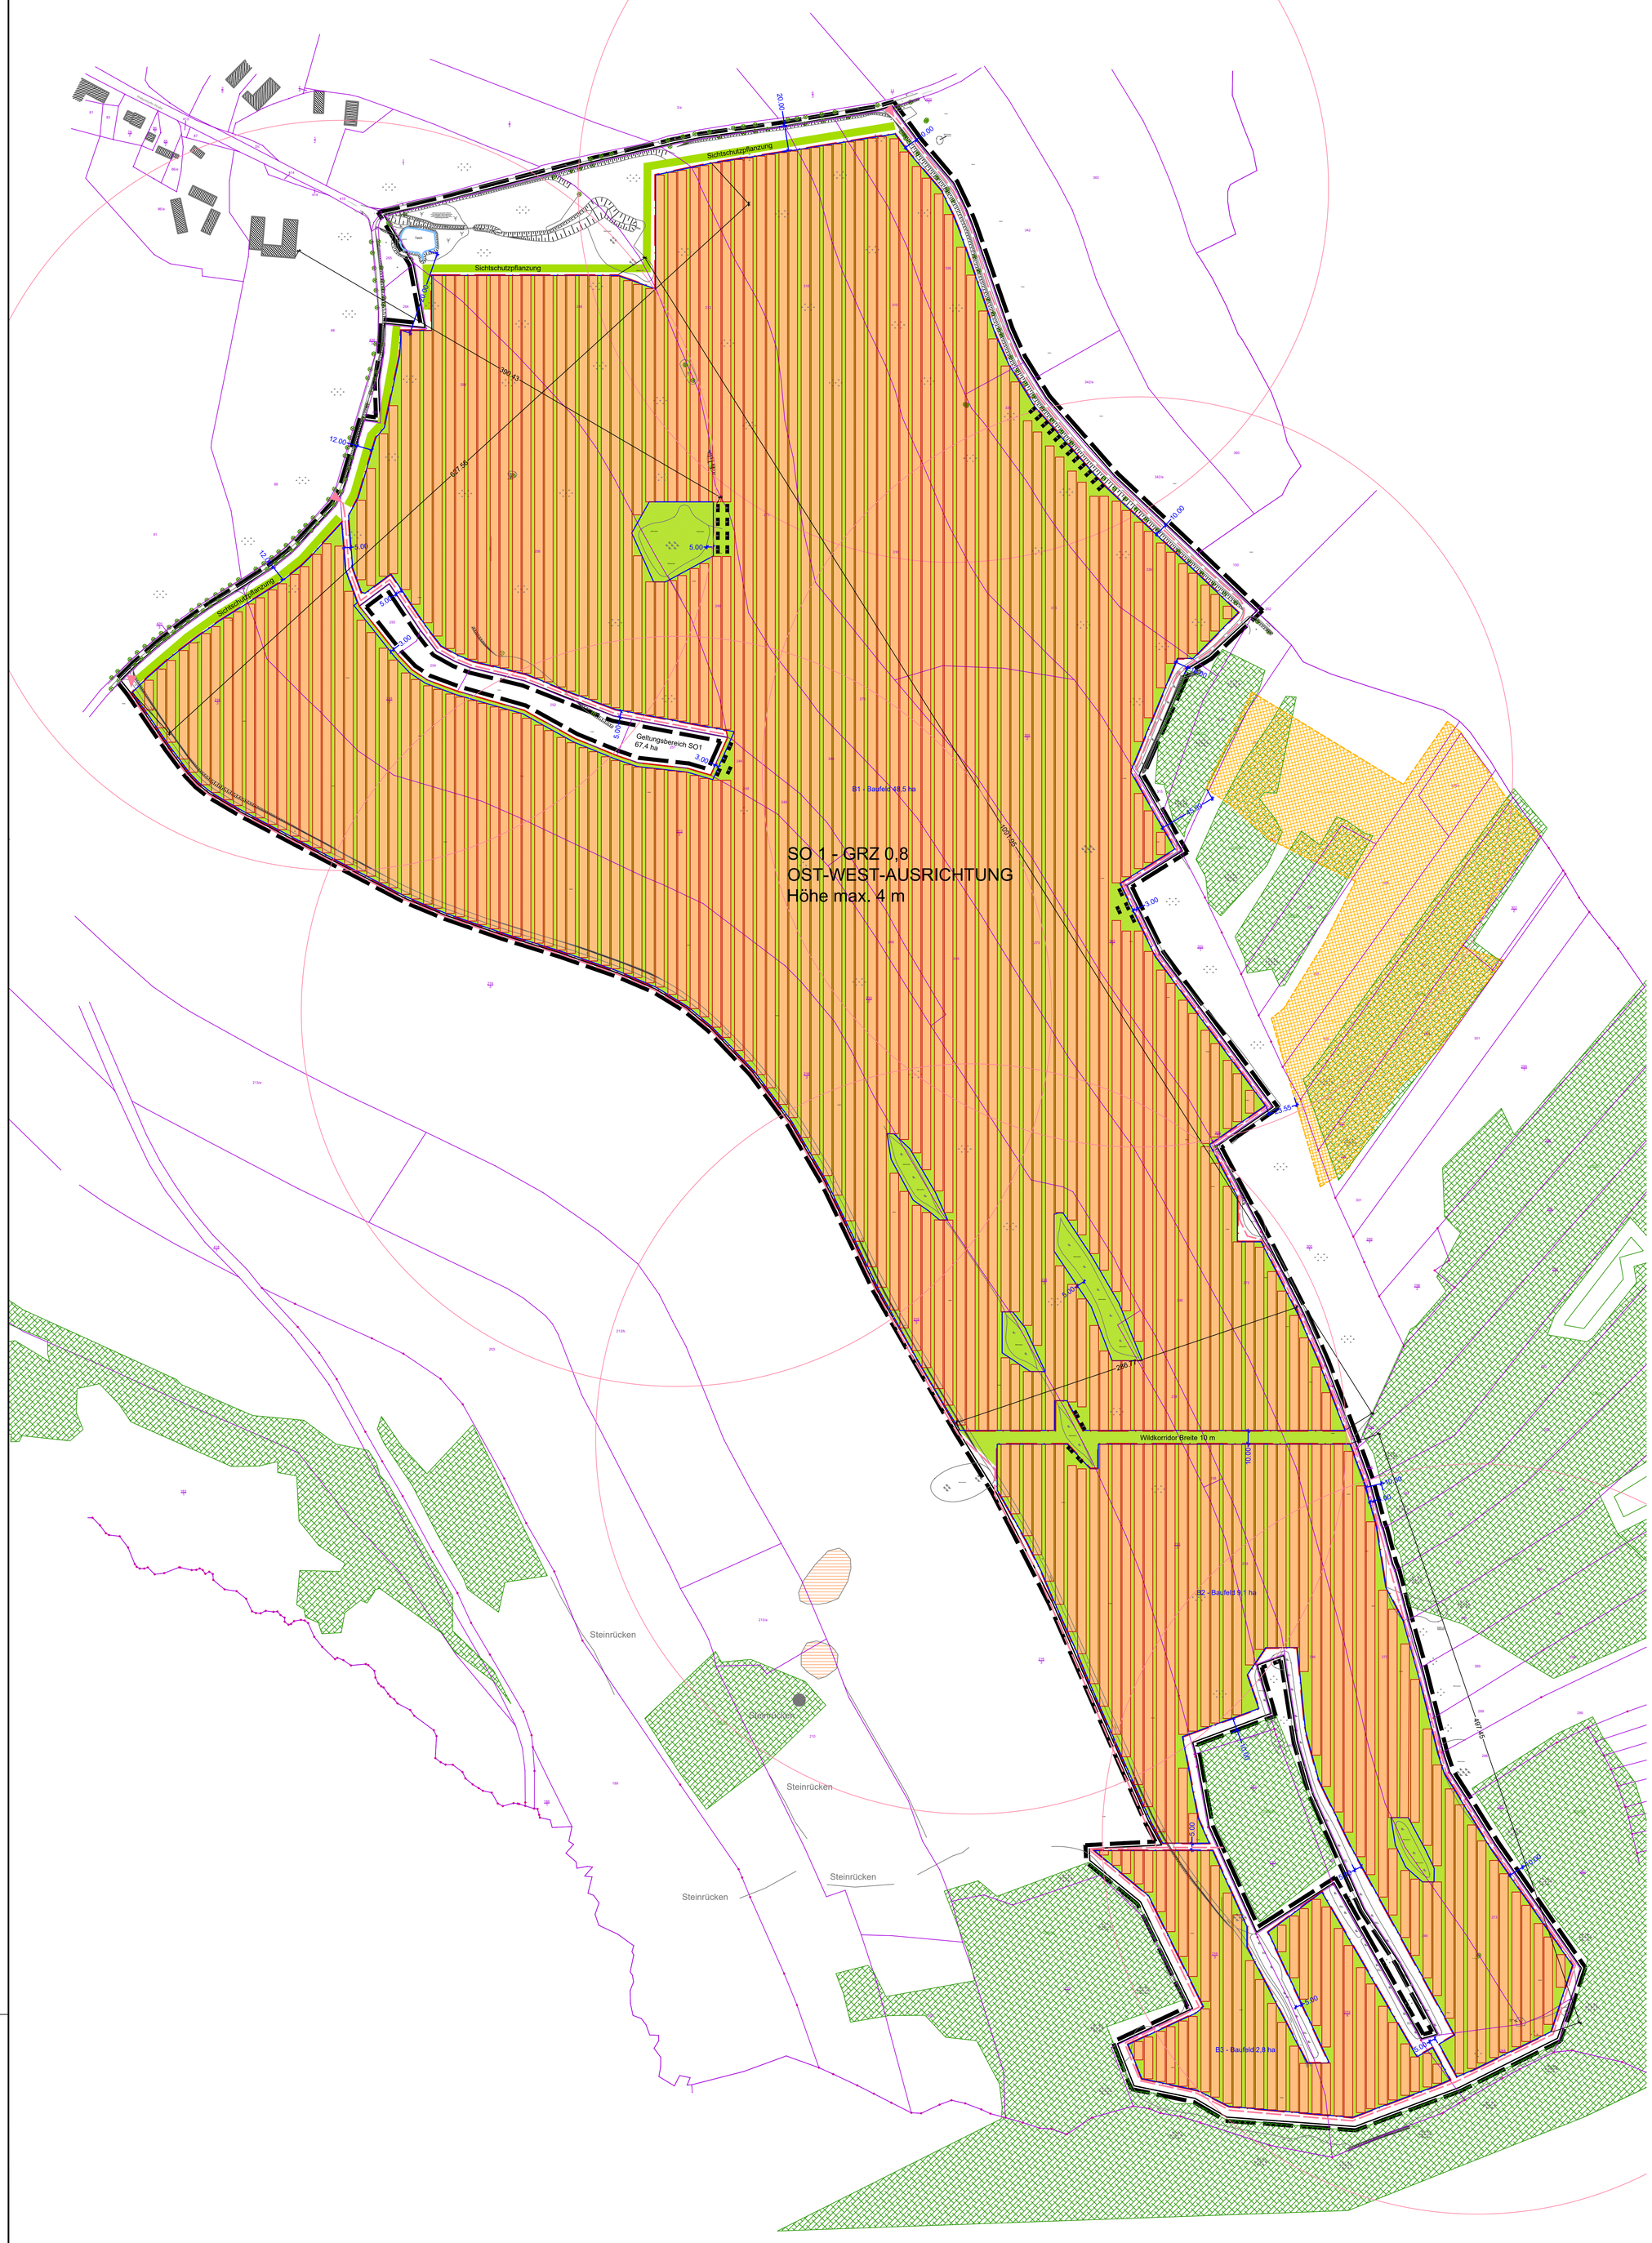

ZEICHENERKLÄRUNG

PHOTOVOLTAIK - FREIFLÄCHENANLAGEN

- Flurstücksgrenze, Flurstücksnummer
- Geltungsbereich
- Baugrenze
- öffentliche Erschließung
- Erschließungswege befestigt
- Löschwasserentnahme Radienschlag 300 m
- PV-Modultische, Höhe max. 4 m siehe Systemdarstellung
- technische Nebenanlagen (Trafos, Batteriespeicher, Wechselrichter)
- Einfriedung - Zaun neu, Höhe max. 3 m
- Baum Bestand
- geschütztes § Biotop
- FND Flächennaturdenkmal
- Wald nach sächs. Waldgesetz
- Dauergrünland im Solarpark
- Neupflanzung freiwachsende Hecken

SOLARPARK WALTERSDORF - BILANZ **Stand 29.08.2025**

Modul:	Leistung Watt:	Maße mm:	Fläche m²:	Ratio W/m²:
Trina Vertex N720W	720	1303 x 2384	3,11	232
Astro N5	650	1134 x 2465	2,79	233
Longi X10 Scientist	**650**	**1134 x 2382**	**2,7**	**241**

Baufeld-Nr. - Belegung	Grundstücks-fläche (m2)	Modulfläche gesamt (m2)	Anzahl Module (gesamt)	Teilleistung (MWp)	GRZ (Modulfläche/ Grundstücks-fläche)
1 - Ost/West (SO 1)	706.818,00	367.537,00	136.124,81	**88,48**	
2 - Ost/West (SO 1)		20.246,00	7.498,52	**4,87**	
3 - Ost/West (SO 1)		66.001,00	24.444,81	**15,89**	
4 - Ost/West (SO 2)	191.545,00	97.089,00	35.958,89	**23,37**	
SUMME	**898.363,00**	**550.873,00**	**204.027,04**	**132,62**	**0,61**

Stand 17.12.2025

NORD

ÄNDERUNGEN	DATUM	INDEX
Sichtschutzhecke, Wald und Flurstück 240 außerhalb Geltungsbereich, Nebenanlagen	02.09.25	B
nördliche Erschließung gefangene Flurstücke SO1	23.09.25	C
Verschiebung Batteriespeicher nach Norden SO1	17.12.25	D

ADRESSE
DÖBRAER BACH
01825 LIEBSTADT OT WALTERSDORF

BAUVORHABEN
SOLARPARK WALTERSDORF

PLANINHALT
GENEHMIGUNGSPLANUNG
VORHABEN- & ERSCHLIESSUNGSPLAN
TEILBEREICH SO 1

PLANNUMMER 1 | INDEX D
PHASE vB-PLAN | BLATTGRÖSSE DIN - A 0
MASSSTAB 1: 2.000 | ZEICHENEINHEITEN METER
GEZEICHNET AF | PLANDATUM 17.12.25
BEARBEITET AF | DATEINAME WALTERSDORF
UNTERSCHRIFT

PLANVERFASSER
P+S Projektentwicklung Solar-Bau GmbH
Südstraße 78 A, 03253 Doberlug-Kirchhain, Deutschland
Tel. 035025 573 330
sekretariat[at]projekt-solartechnik.de
Amtsgericht Cottbus, HRB 15058

BAUHERR / VORHABENSTRÄGER
Solarpark Waltersdorf GmbH Co. KG
Waltersdorfer Str. 1, 01825 Liebstadt, Deutschland

BESTÄTIGT: DATUM, UNTERSCHRIFT

Kartendaten: © OpenStreetMap-Mitwirkende, SRTM | Kartendarstellung: © OpenTopoMap (CC-BY-SA)

VORHABEN- UND ERSCHLIESSUNGSPLAN
ZUM vB-PLAN "SOLARPARK WALTERSDORF" - SO 2 (M 1: 2.000)

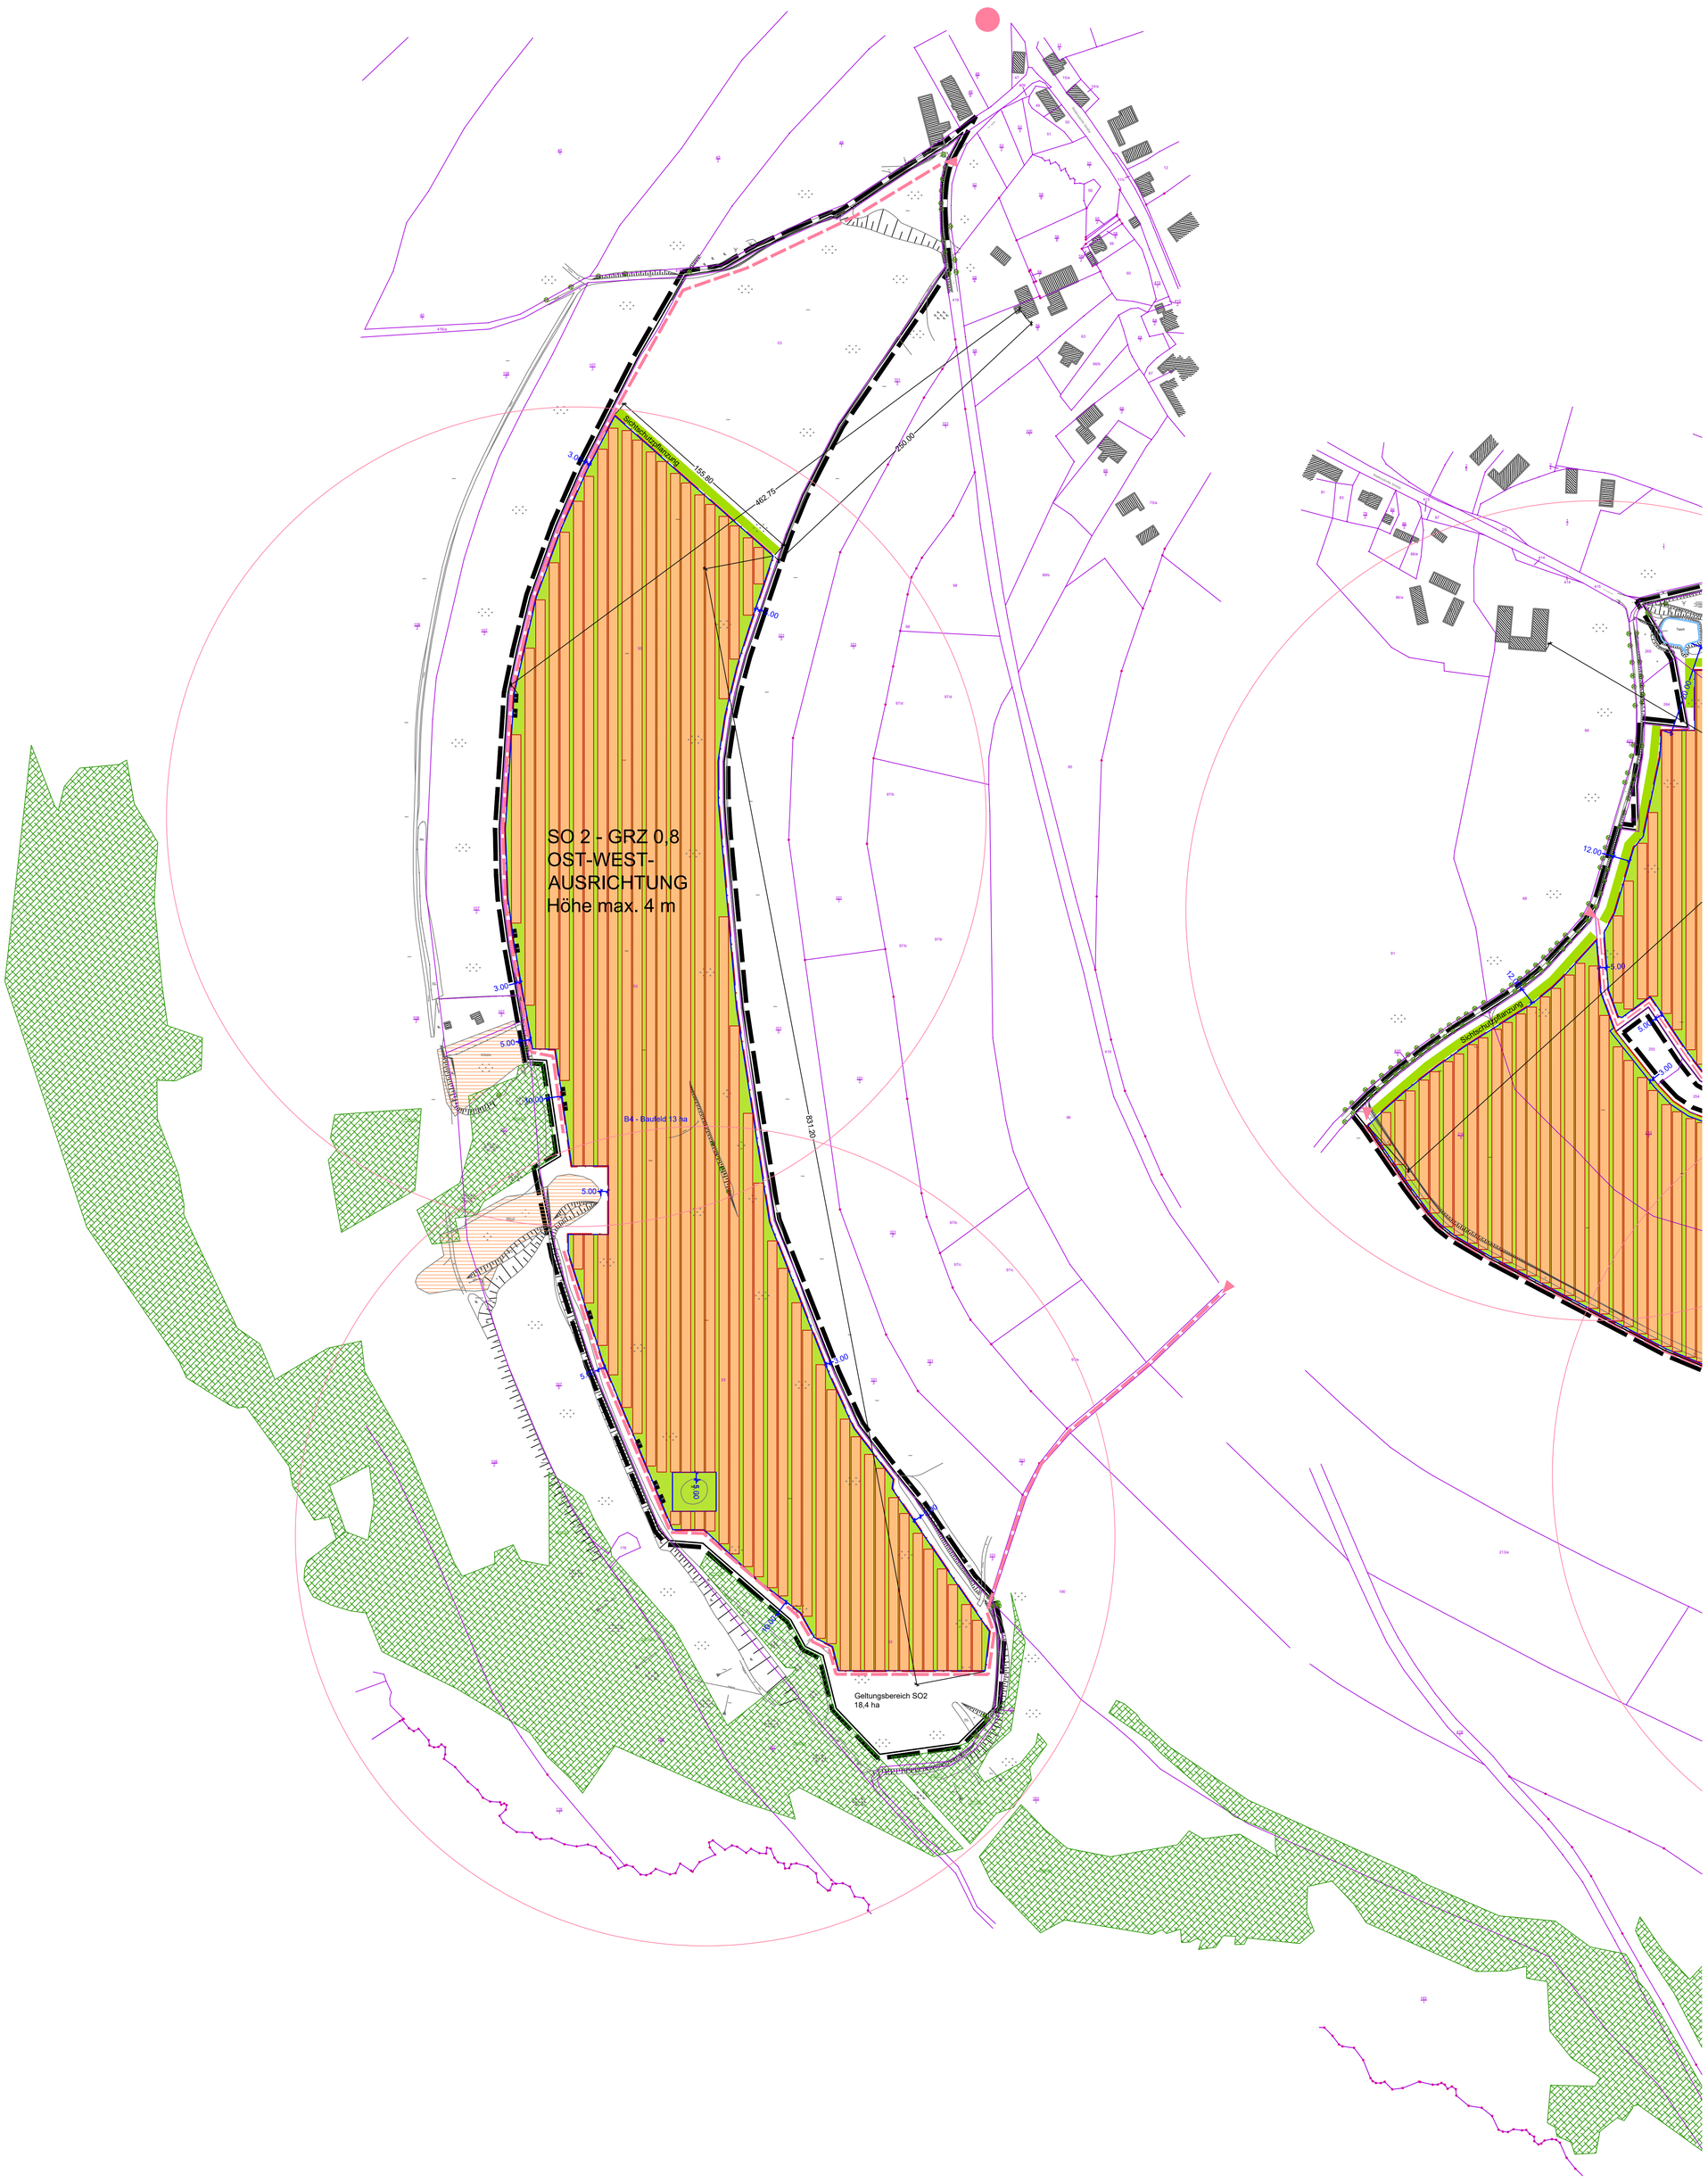

ZEICHENERKLÄRUNG

PHOTOVOLTAIK - FREIFLÄCHENANLAGEN

- Flurstücksgrenze, Flurstücksnummer
- Geltungsbereich
- Baugrenze
- öffentliche Erschließung
- Erschließungswege befestigt
- Löschwasserentnahme Radienschlag 300 m
- PV-Modultische, Höhe max. 4 m siehe Systemdarstellung
- technische Nebenanlagen (Trafos, Batteriespeicher, Wechselrichter)
- Einfriedung - Zaun neu, Höhe max. 3 m
- Baum Bestand
- geschütztes § Biotop
- FND Flächennaturdenkmal
- Wald nach sächs. Waldgesetz
- Dauergrünland im Solarpark
- Neupflanzung freiwachsende Hecken

SOLARPARK WALTERSDORF - BILANZ **Stand 29.08.2025**

Modul:	Leistung Watt:	Maße mm:	Fläche m²:	Ratio W/m²:
Trina Vertex N720W	720	1303 x 2384	3,11	232
Astro N5	650	1134 x 2465	2,79	233
Longi X10 Scientist	**650**	**1134 x 2382**	**2,7**	**241**

Baufeld-Nr. - Belegung	Grundstücks-fläche (m2)	Modulfläche gesamt (m2)	Anzahl Module (gesamt)	Teilleistung (MWp)	GRZ (Modulfläche/ Grundstücks-fläche)
1 - Ost/West (SO 1)	706.818,00	367.537,00	136.124,81	**88,48**	
2 - Ost/West (SO 1)		20.246,00	7.498,52	**4,87**	
3 - Ost/West (SO 1)		66.001,00	24.444,81	**15,89**	
4 - Ost/West (SO 2)	191.545,00	97.089,00	35.958,89	**23,37**	
SUMME	**898.363,00**	**550.873,00**	**204.027,04**	**132,62**	**0,61**

Stand 17.12.2025

ÄNDERUNGEN	DATUM	INDEX
Sichtschutzhecke, Wald und Flurstück 240 außerhalb Geltungsbereich, Nebenanlagen	02.09.25	B
nördliche Enschließung gefangene Flurstücke SO1	23.09.25	C
Verschiebung Batteriespeicher nach Norden SO1	17.12.25	D

ADRESSE
DÖBRAER BACH
01825 LIEBSTADT OT WALTERSDORF

BAUVORHABEN
SOLARPARK WALTERSDORF

PLANINHALT
GENEHMIGUNGSPLANUNG
VORHABEN- & ERSCHLIESSUNGSPLAN
TEILBEREICH SO 2

PLANNUMMER	INDEX
2	D
PHASE: vB-PLAN	BLATTGRÖSSE: DIN - A 0
MASSSTAB: 1: 2.000	ZEICHENEINHEITEN: METER
GEZEICHNET: AF	PLANDATUM: 17.12.25
BEARBEITET: AF	DATEINAME: WALTERSDORF
UNTERSCHRIFT	

PLANVERFASSER
P+S Projektentwicklung Solar-Bau GmbH
Südstraße 78 A, 03253 Doberlug-Kirchhain, Deutschland
Tel. 035025 573 330
sekretariat[at]projekt-solartechnik.de
Amtsgericht Cottbus, HRB 15038

BAUHERR / VORHABENSTRÄGER
Solarpark Waltersdorf GmbH & Co. KG
Waltersdorfer Str. 1, 01825 Liebstadt, Deutschland

BESTÄTIGT: DATUM, UNTERSCHRIFT

Kartendaten: © OpenStreetMap-Mitwirkende, SRTM | Kartendarstellung: © OpenTopoMap (CC-BY-SA)